




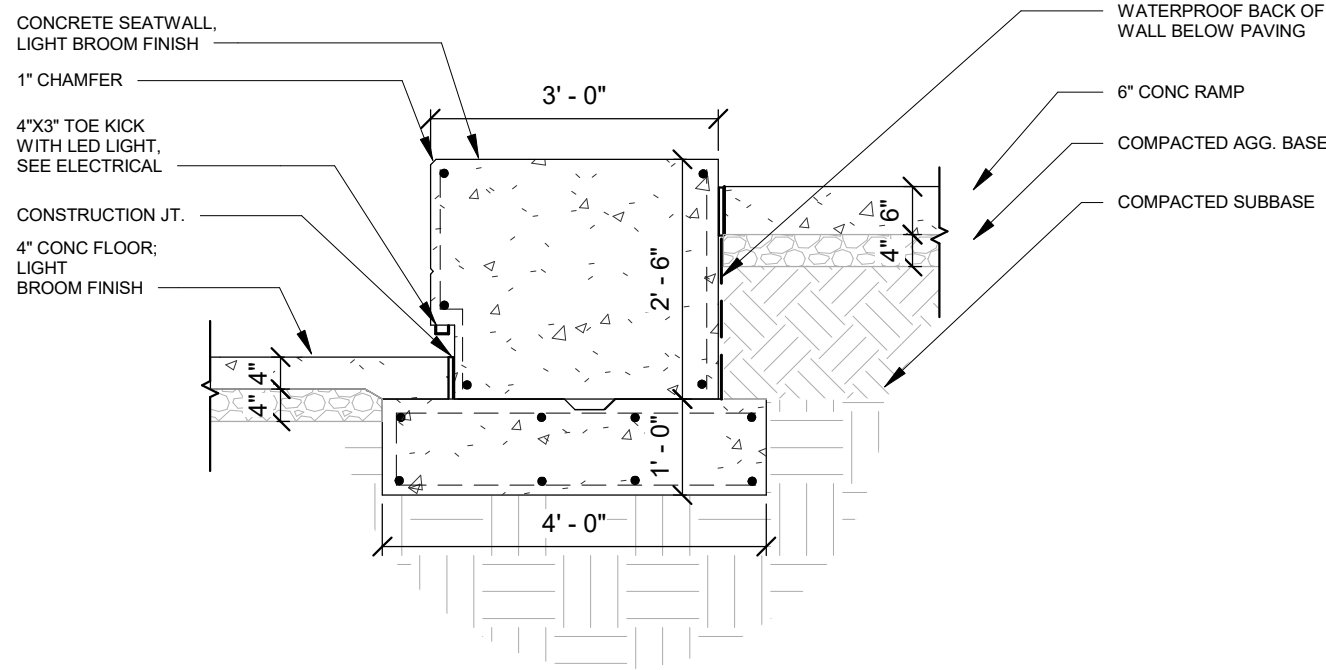


F3 SEATWALL DETAIL
1/2" = 1'-0"

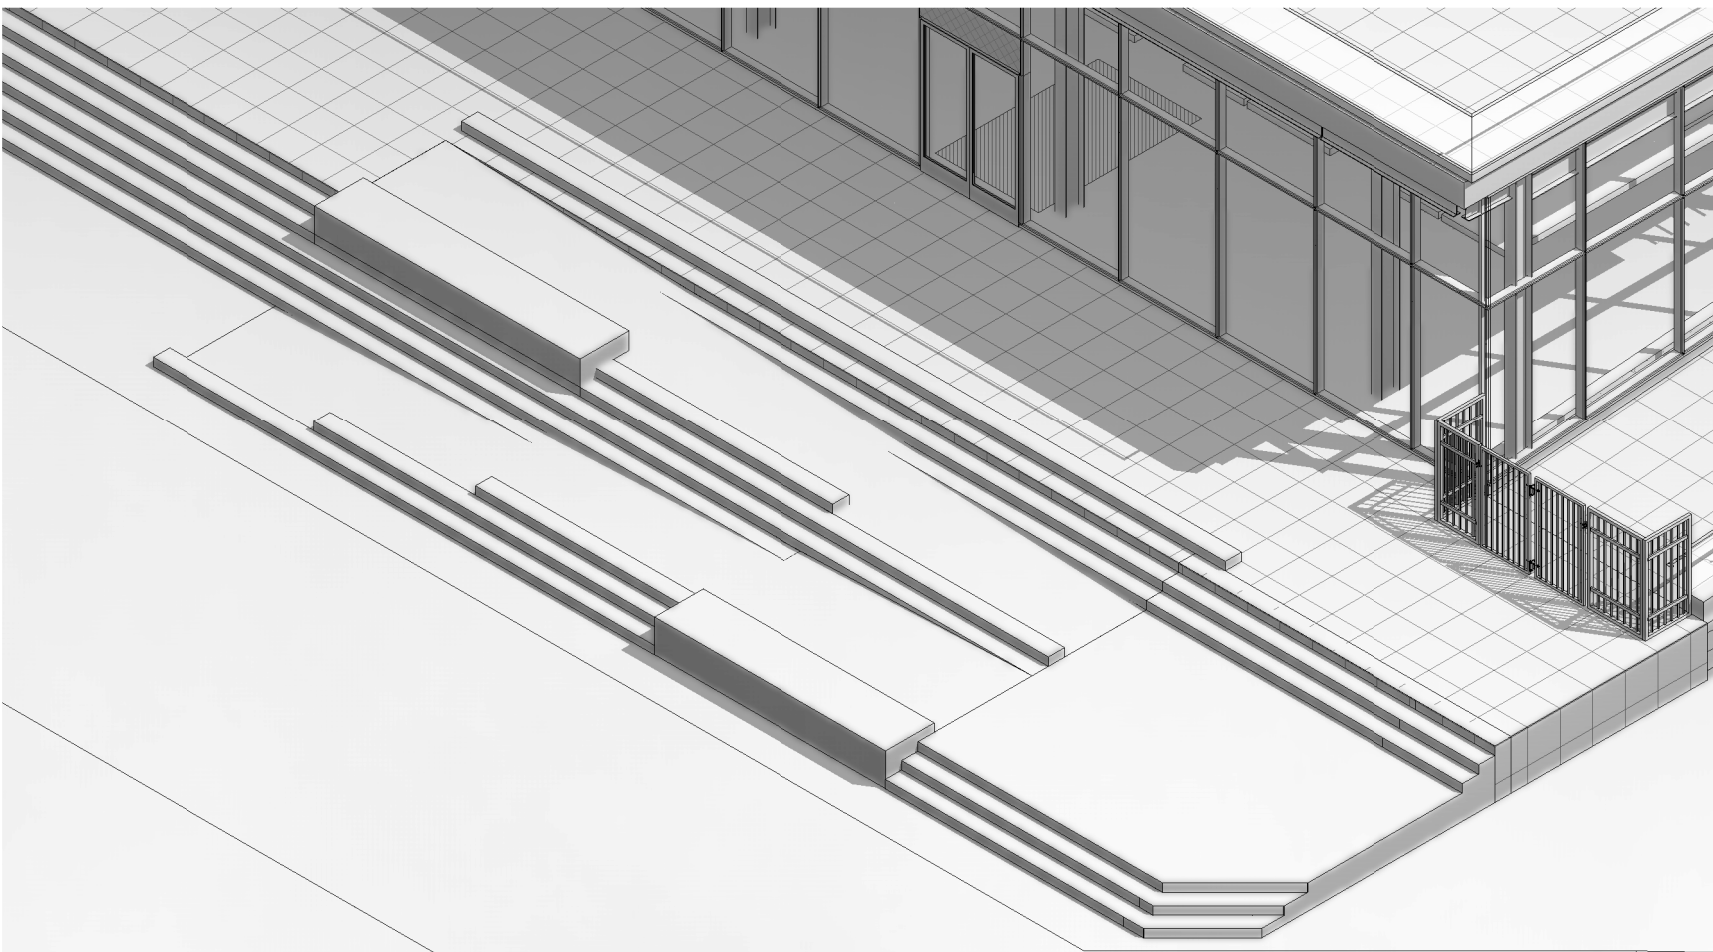


F6 STRAMP ISOMETRIC

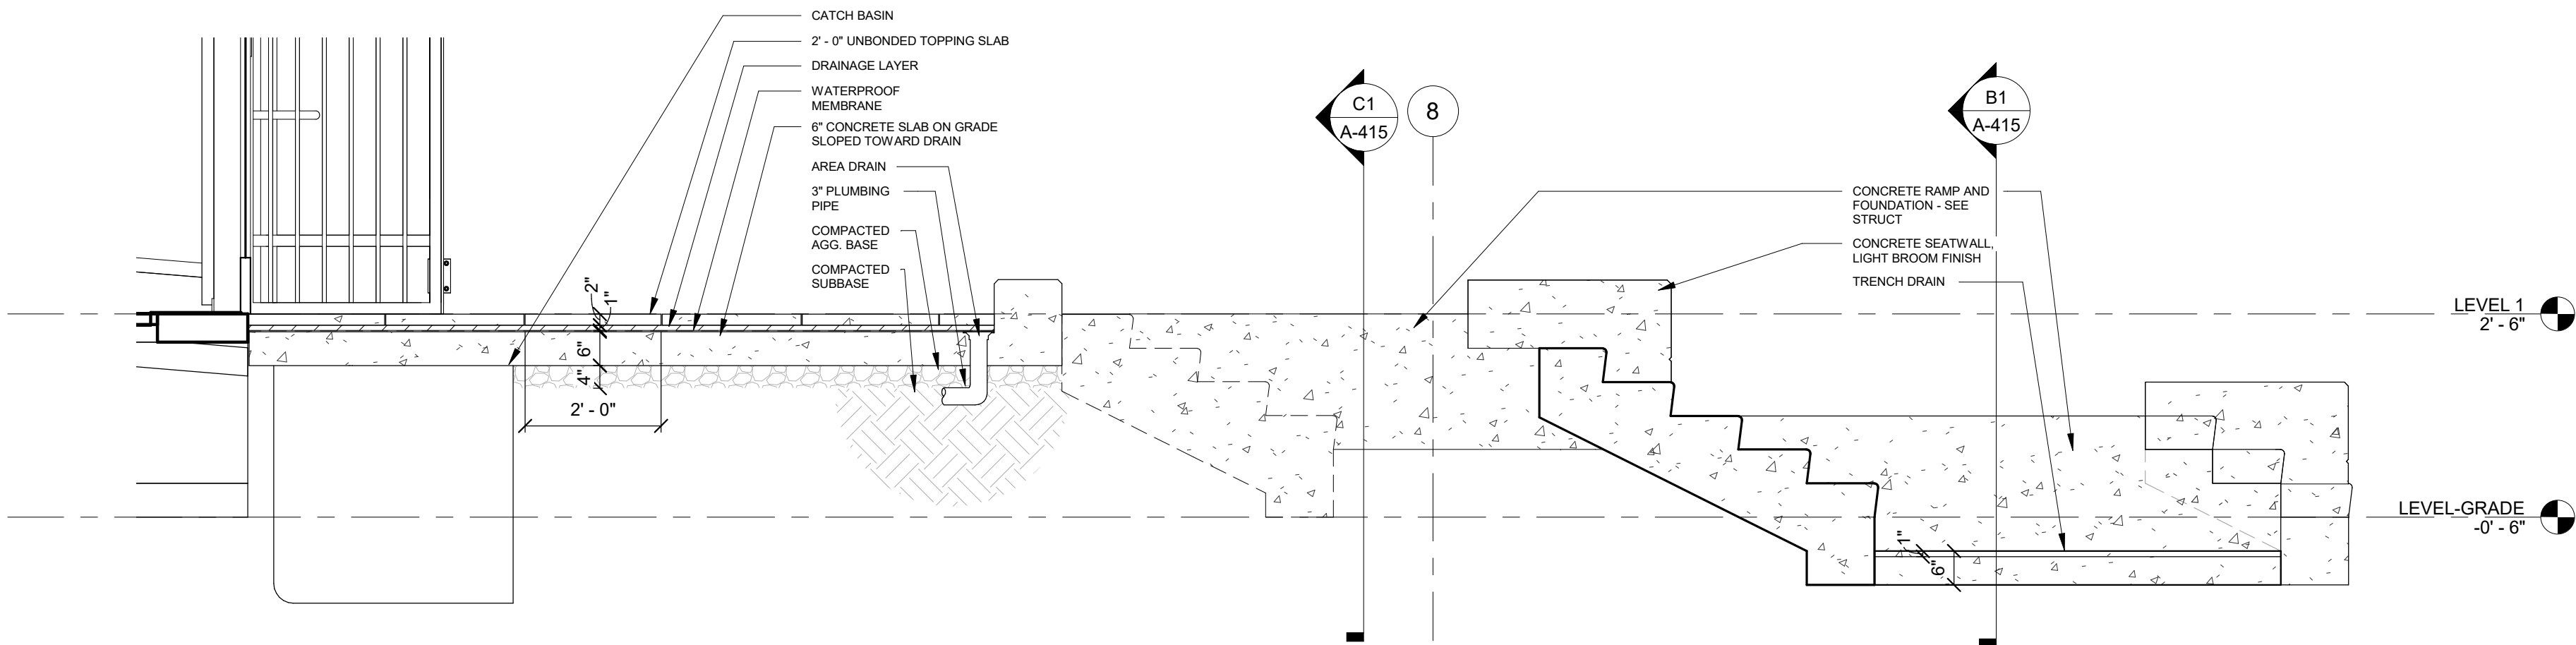

C3 TRANSVERSE SECTION WEST STRAMP
1/2" = 1'-0"

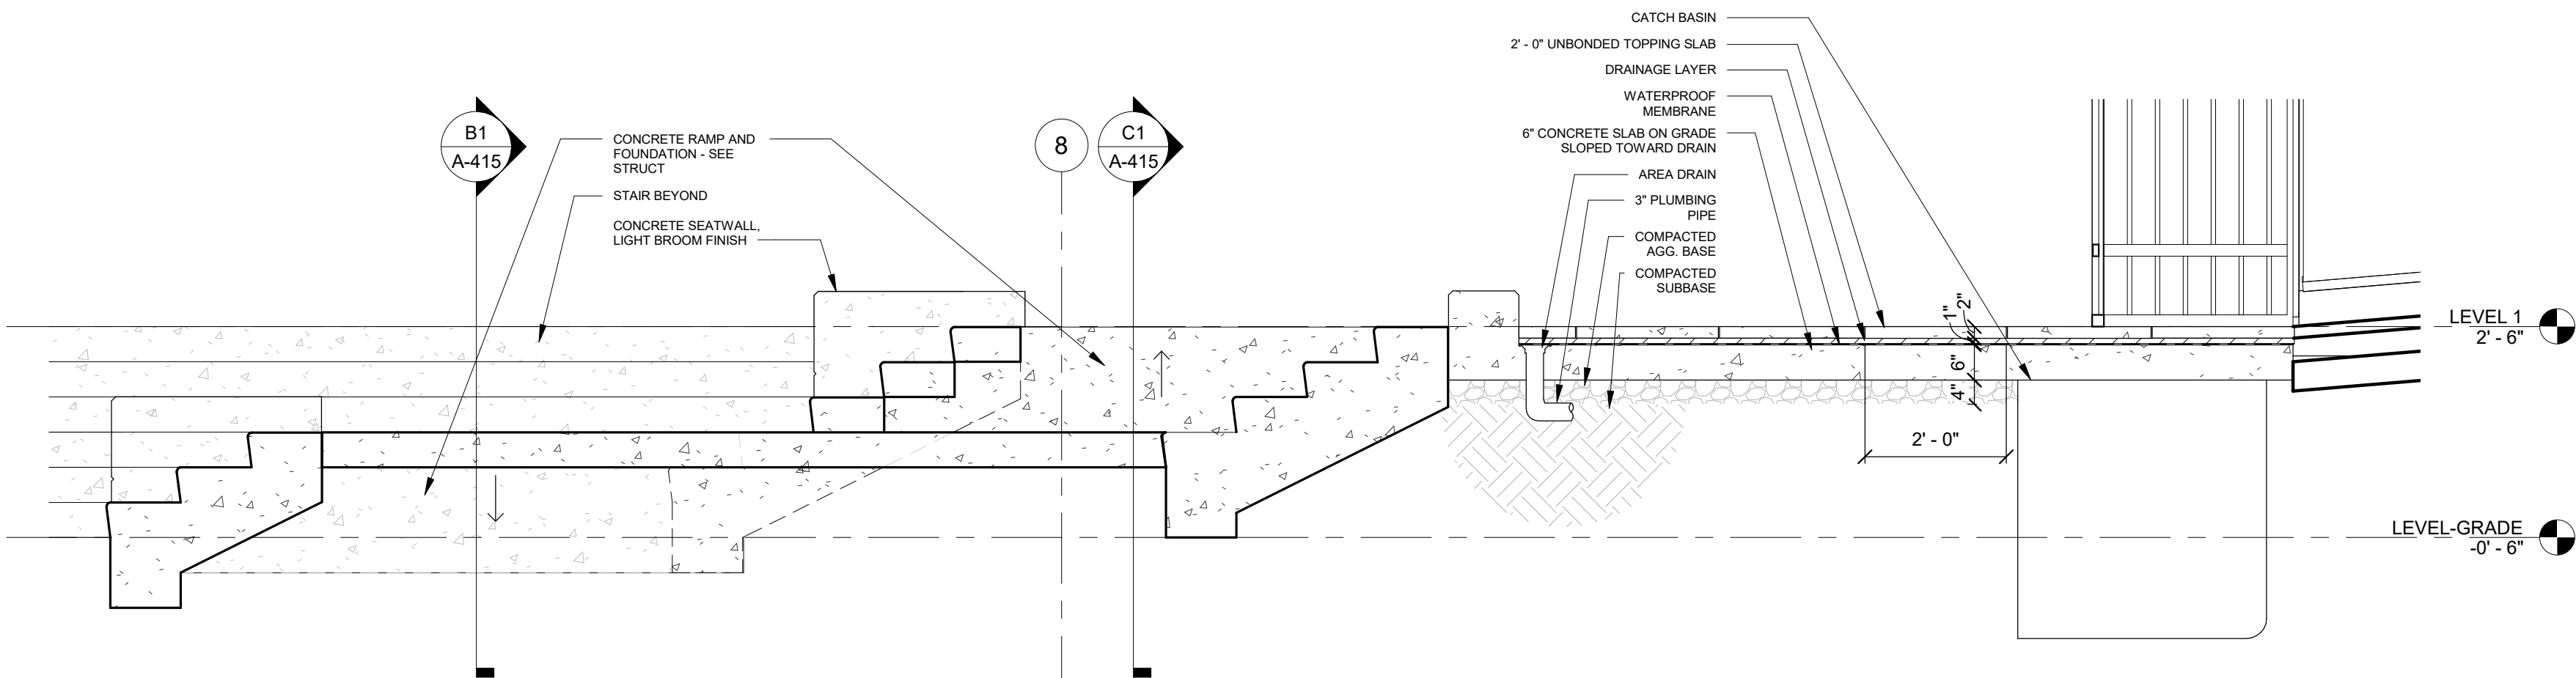

A3 TRANSVERSE SECTION EAST STRAMP
1/2" = 1'-0"

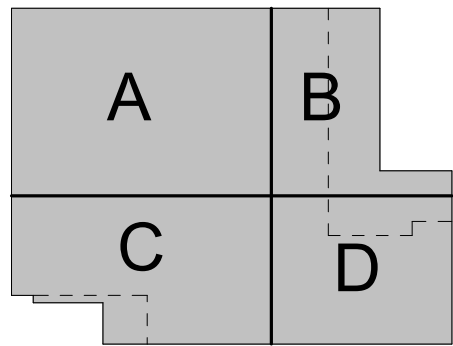

KEY PLAN



US Army Corps
of Engineers®

MARK	DESCRIPTION	DATE

DESIGNED BY: N RADISC	ISSUE DATE: AUGUST 2024
DRAWN BY:	SOLICITATION NO.:
CHECKED BY:	CONTRACT NO.:
SUBMITTED BY: EXP FEDERAL	W812HN21D200
FILE NAME: PN-88727-ARCH-REV4.rvt	
SIZE: ANSI D	

US ARMY CORPS OF ENGINEERS
SAVANNAH DISTRICT
100 W. Oglethorpe Ave
Savannah, GA 31401

205 N. MICHIGAN AVE
CHICAGO, IL 60601
proj. no.: CHL22021869-A0

exp.federal

FORT EISENHOWER, GEORGIA MCA4: CYBER INSTRUCTIONAL FACILITY CLASSROOMS AND AUDITORIUM FY25 PN 88727 ARCHITECTURAL EXTERIOR STAIR DETAILS

SHEET ID A-416
